


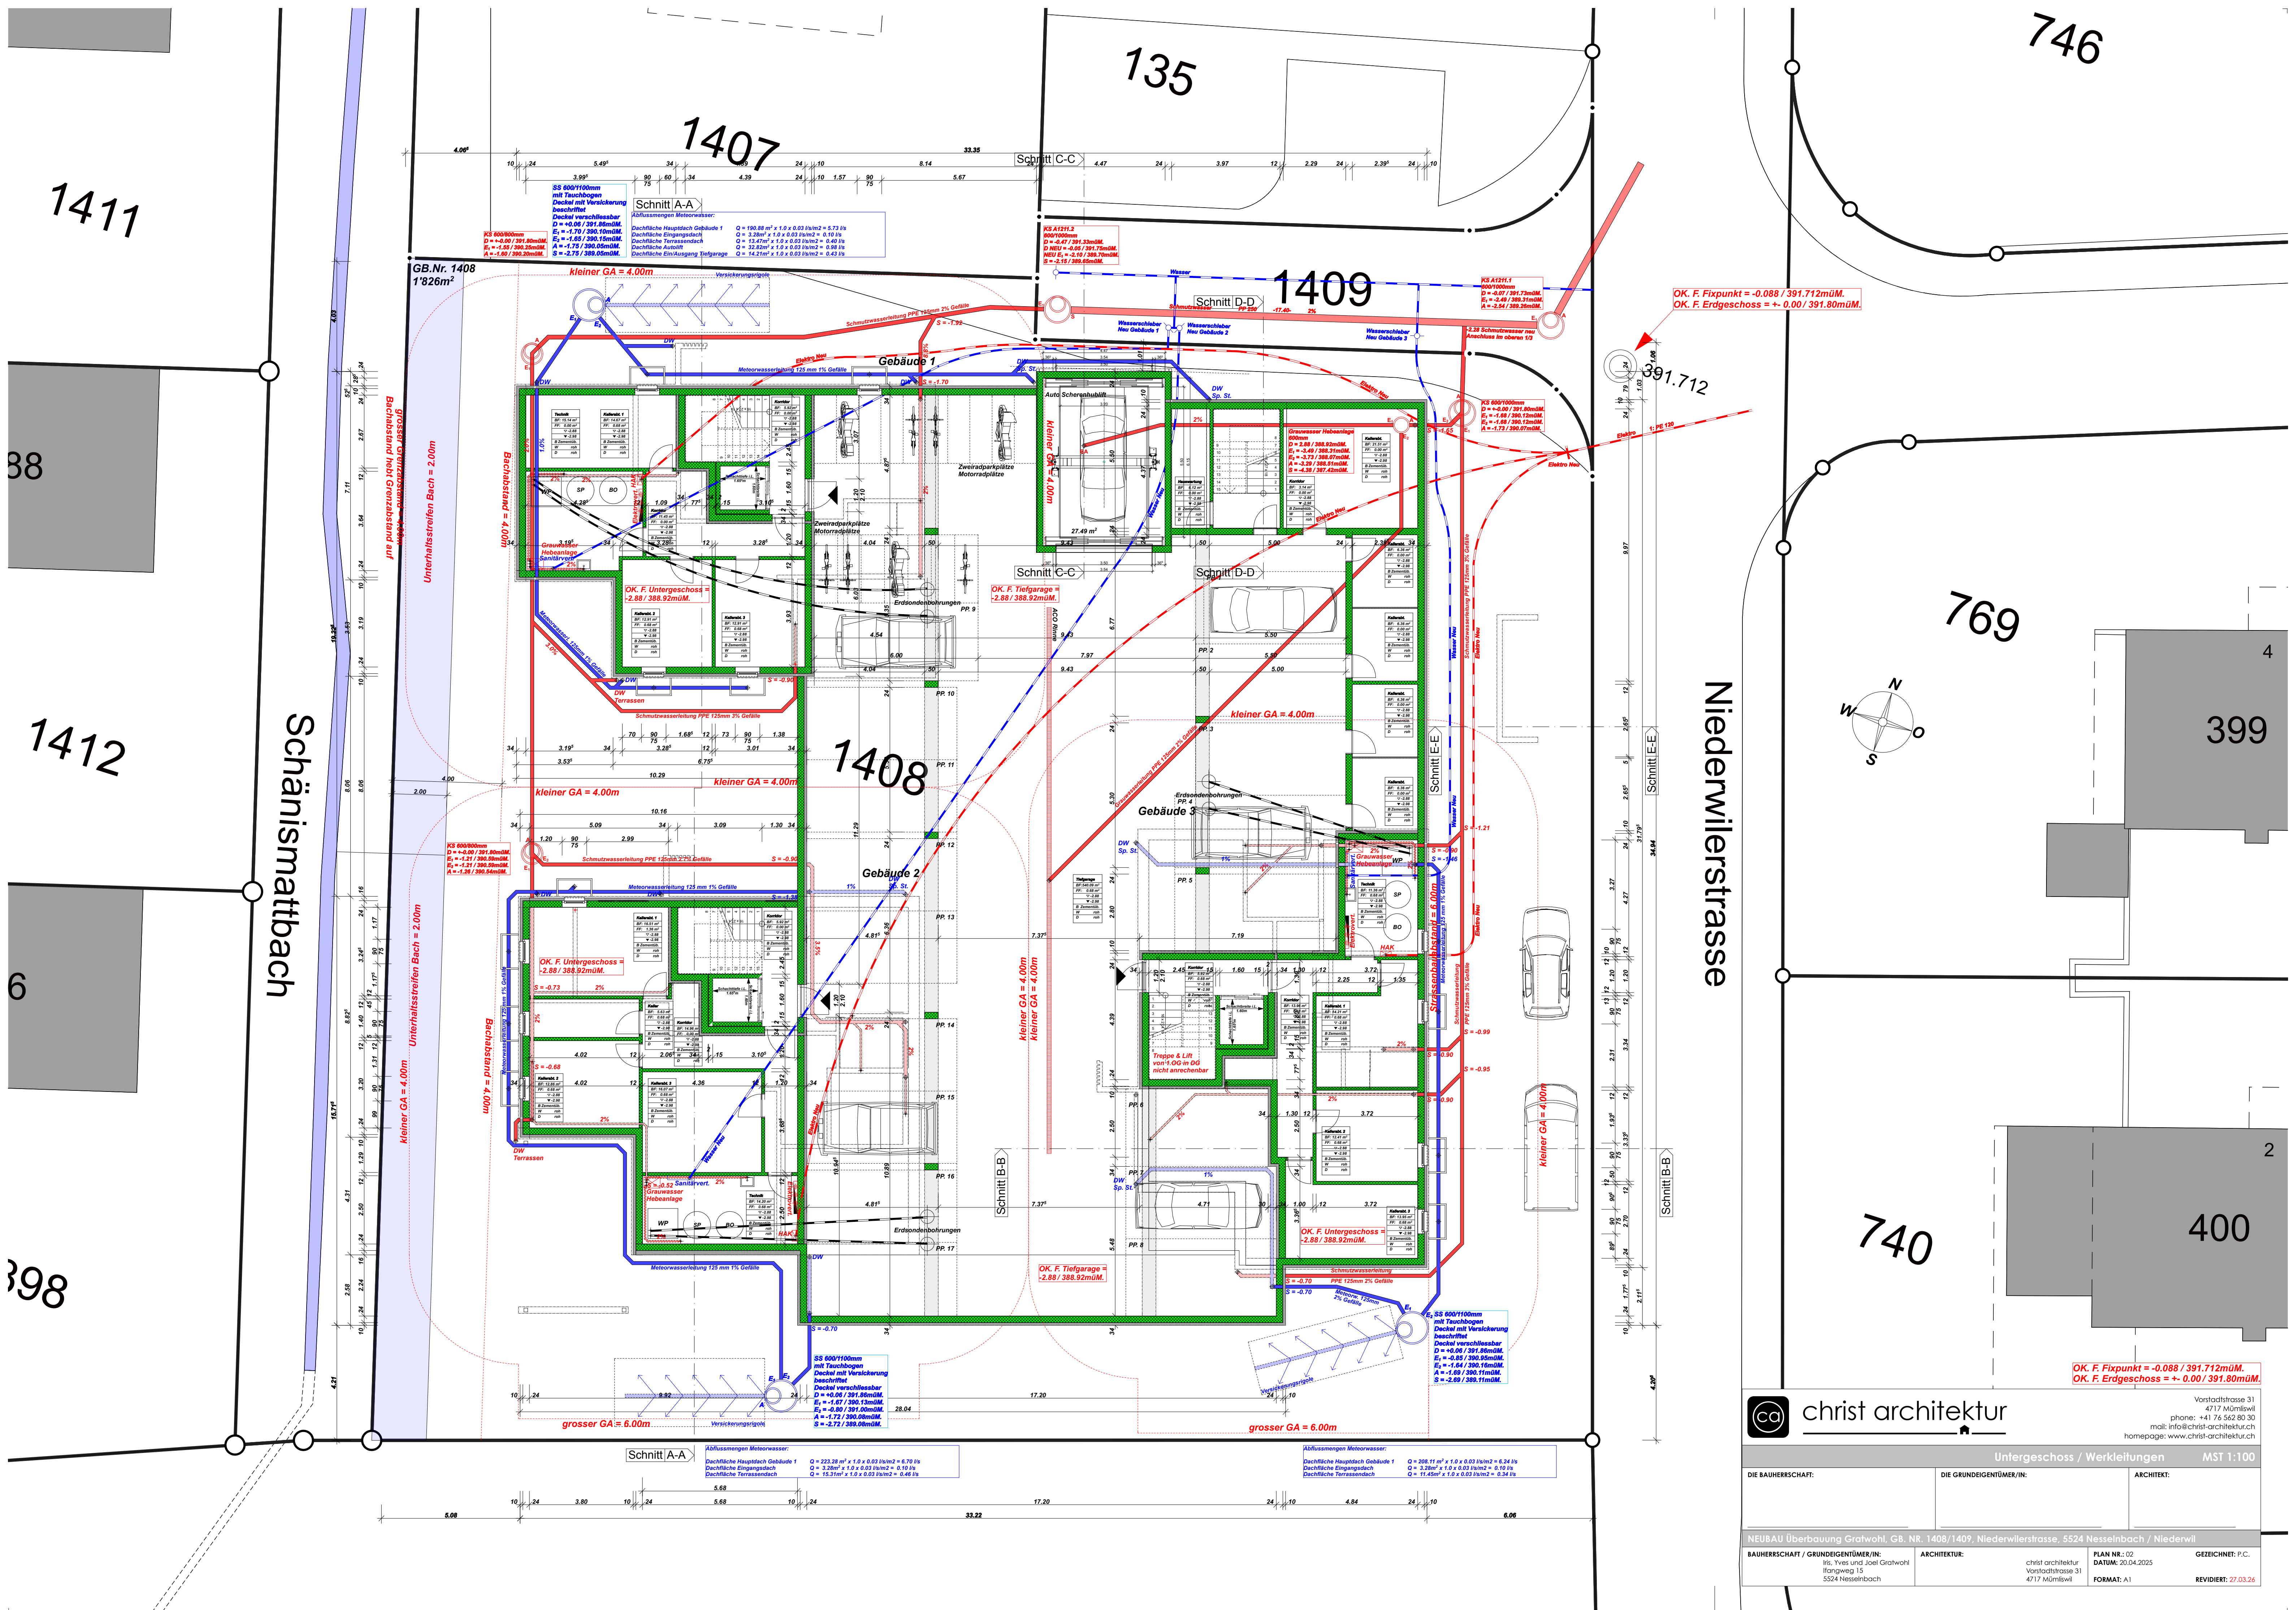



christ architektur

NEUBAU Überbauung Gratwohl, GB. NR. 1408/1409, Niedervilerstrasse, 5524 Nesselbach / Niederwil

BAUHERRSCHAFT / GRUNDEIGENTÜMER/IN:
Mrs. Yves und Joel Gratwohl
Ifanweg 15
5524 Nesselbach

ARCHITEKT:
christ architektur
Vorstadtstrasse 31
4717 Mümliswil

PLAN NR.: 02
DATUM: 20.04.2025
FORMAT: A1

GEZEICHNET: P.C.
REVIDIERT: 27.03.26

Untergeschoss / Werkleitungen

MST 1:100